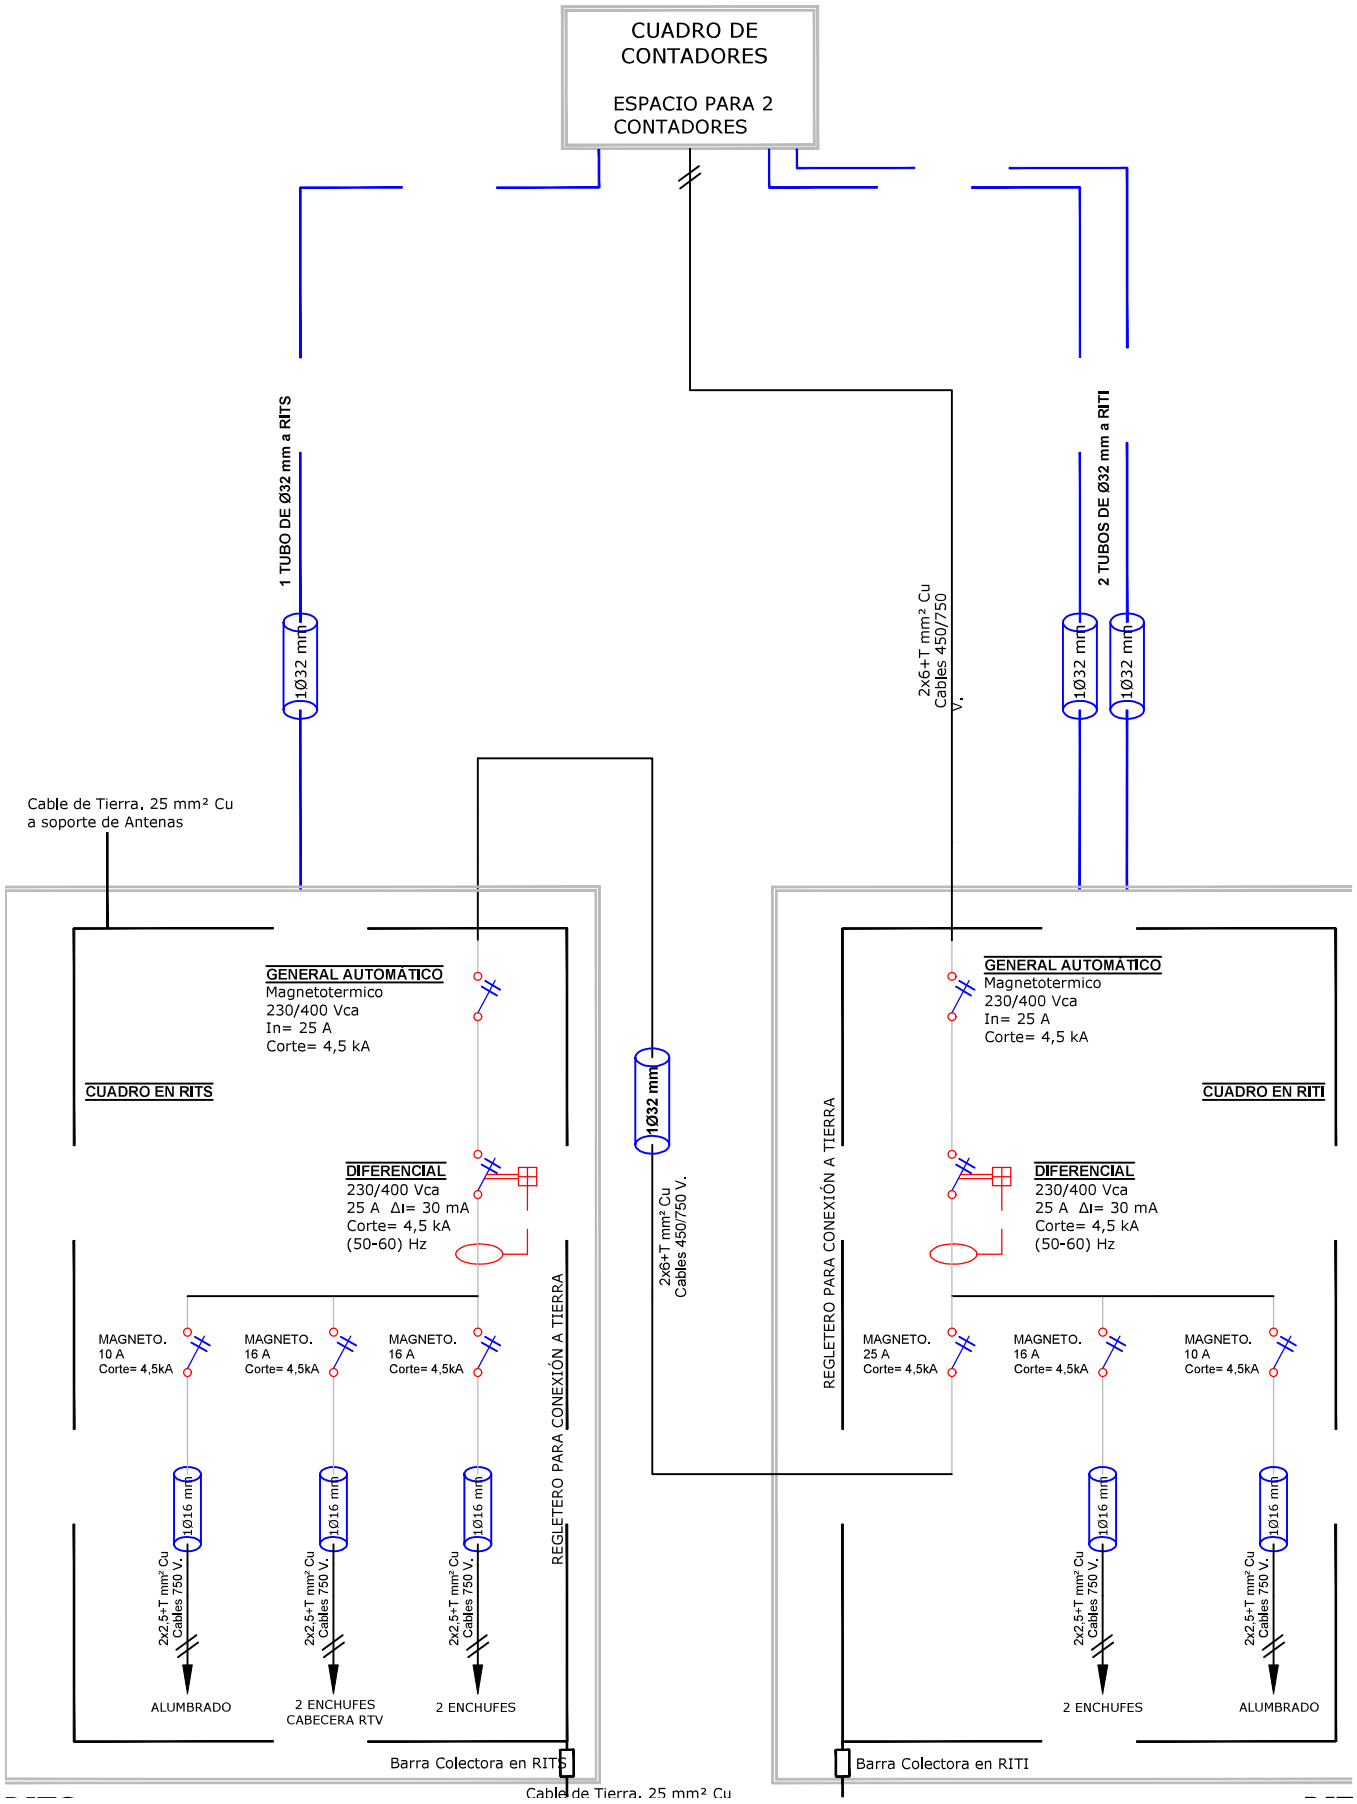



Plano Nº: 2.3.G
Escala: S/E
Revisión: 0

Proyecto de ICT para: 92 viviendas 2 locales y 3 locales comunitarios.
Promotor: NEINOR PENINSULA S.L.U.
Situación: PARCELA RE A4, BOLUETA
48004 BILBAO. (BIZKAIA)

Fecha: 10/07/2023
Ingeniero de Telecomunicación: Gorka Leal Irastorza (Colegiado nº 8599)

A4

IP21ingeniería. Plaza Eihera, 5 Bajo. 20305 IRUN (GUIPUZCOA). Tfn: 943.660047 / 943.619416 www.ip21ingenieria.com / e-mail: tecnico@ip21ingenieria.com